


NOTICE: THIS DRAWING HAS NOT BEEN PUBLISHED AND IS THE SOLE PROPERTY OF FLUOR. AND IS LENT TO THE BORROWER FOR THEIR CONFIDENTIAL USE ONLY, AND IN CONSIDERATION OF THE LOAN OF THIS DRAWING, THE BORROWER PROMISES AND AGREES TO RETURN IT UPON REQUEST AND AGREES THAT IT WILL NOT BE REPRODUCED, COPIED, LENT, OR OTHERWISE DISPOSED OF DIRECTLY OR INDIRECTLY, NOR USED FOR ANY PURPOSE OTHER THAN THAT FOR WHICH IT IS FURNISHED.

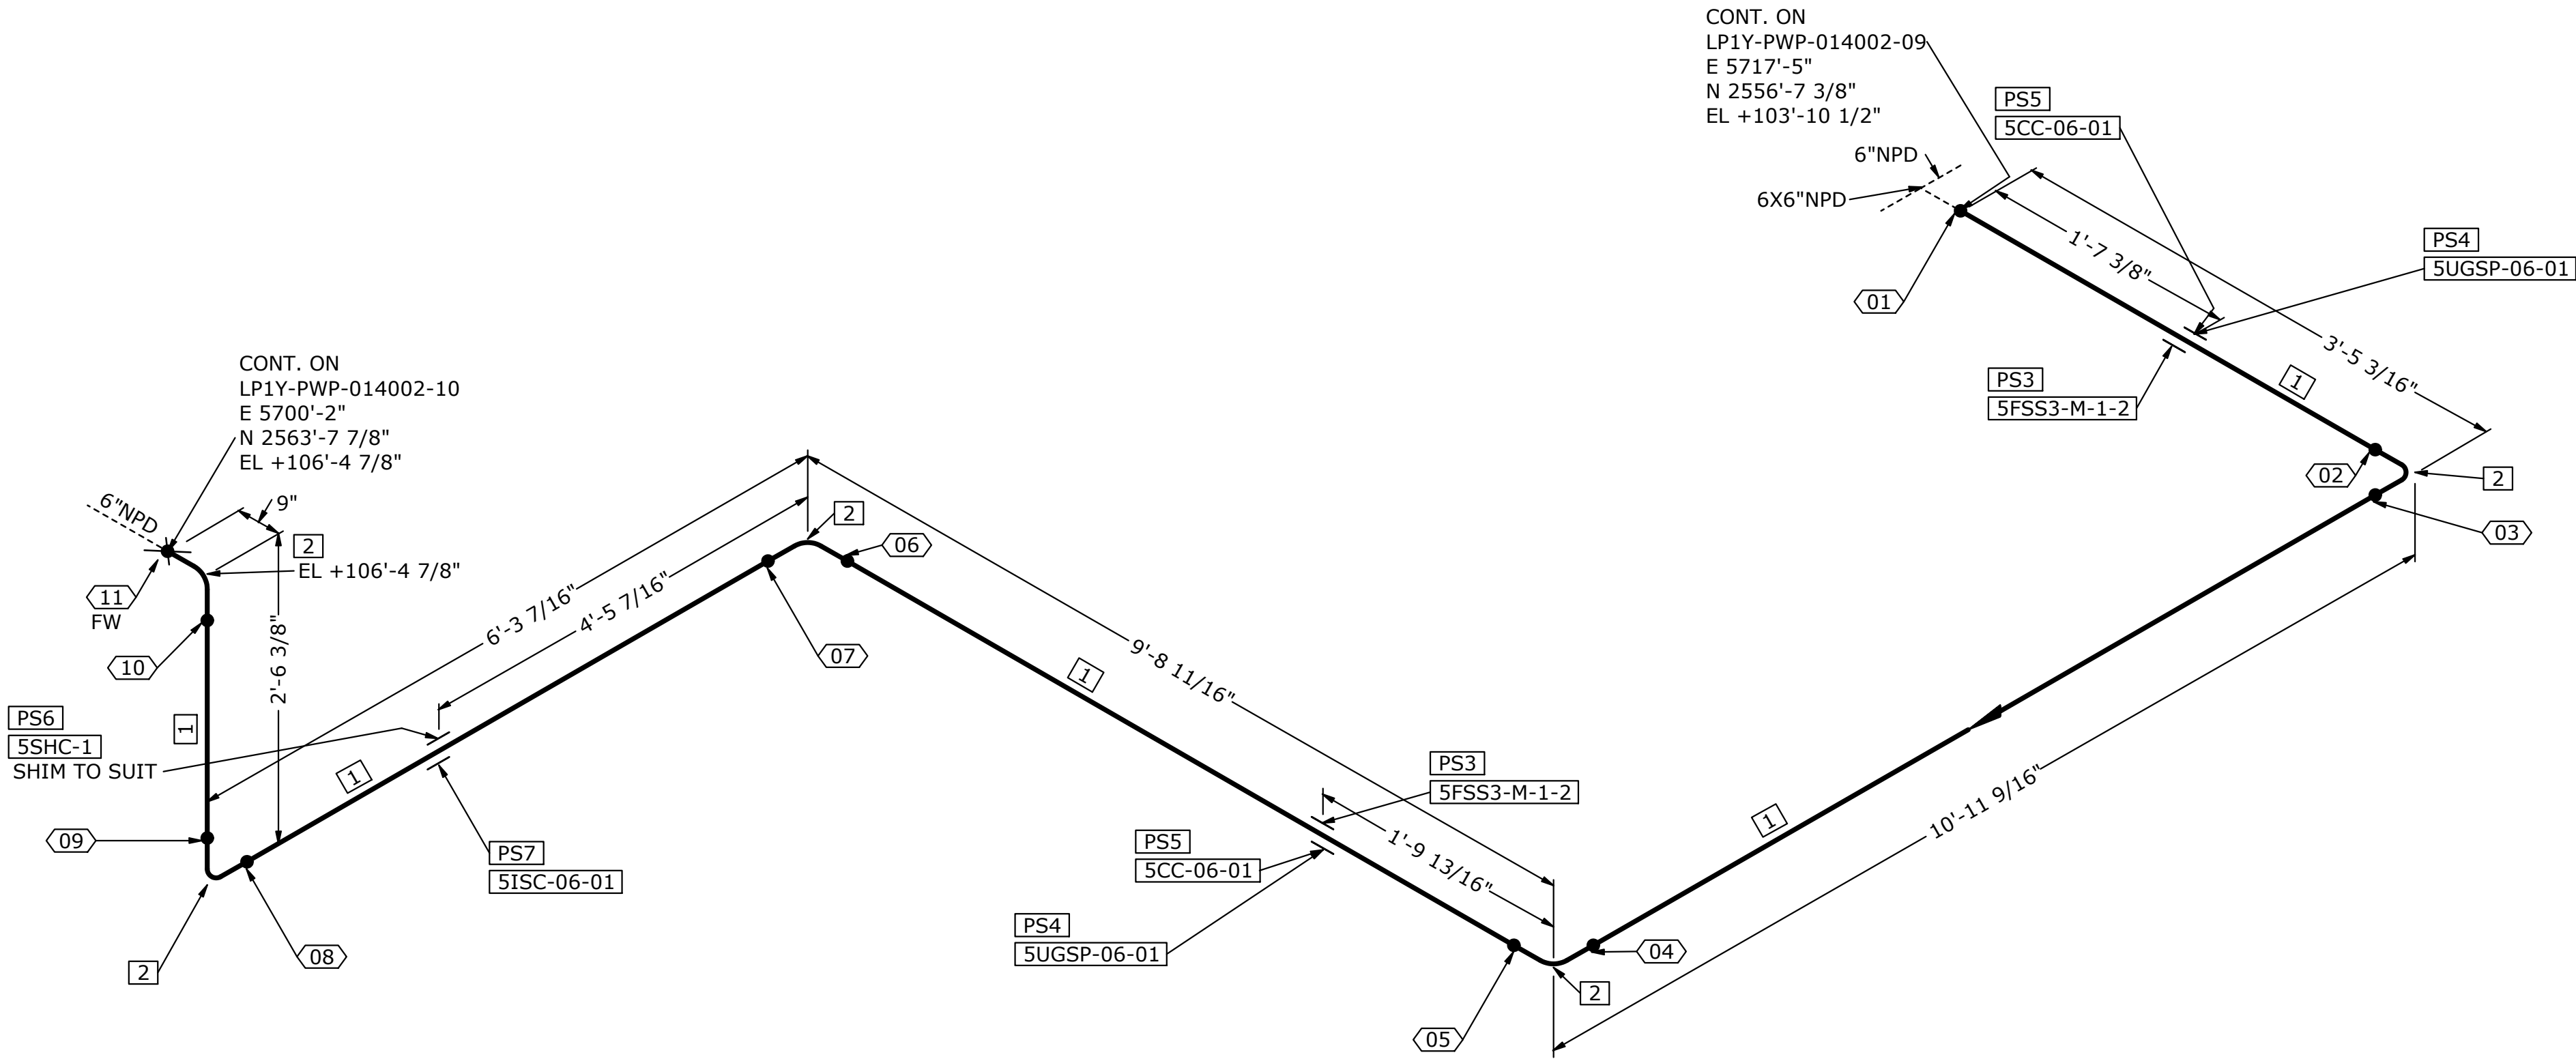

BILL OF MATERIALS

PT NO	DESCRIPTION	NPD (IN)	CMDTY CODE	QTY
1	PIPE SCH 10S ERW 316/316L SS A312	6	5368751	26.2'
2	ELL 90 LR SCH 10S 316/316L SS A403-W	6	5450706	5
3	5FSS3, FIELD SUPPORT, U-FRAME, SIZE M, LC 1, HC 2	6	5FSS3-M-1-2	2
4	5UGSP, U-BOLT GUIDE FOR INSULATED LINES 6" PIPE W/ 1" INSUL	6	5UGSP-06-01	2
5	5CC, SUPPORT CRADLE COLD SERVICE 6" PIPE, 1" INS	6	5CC-06-01	2
6	5SHC, SPACER FOR SLOPED, COLD INSULATED PIPE SIZE 6" AND SMALLER	6	5SHC-1	1
7	5ISC, INSULATED SUPPORT COLD SERV, 6" PIPE W/ 1" INSUL	6	5ISC-06-01	1

- GENERAL NOTE:
- REFER TO THE PIPING LINE LIST FOR PROCESS DATA/CONDITIONS AND OTHER FABRICATION DETAILS SUCH AS TESTING, CLEANING, AND PAINTING REQUIREMENTS.
 - UNLESS OTHERWISE NOTED, ALL WELDS ARE INDICATED AS SHOP WELDS. CONTRACTOR TO DETERMINE FIELD WELDS LOCATIONS AND DOCUMENT ACCORDINGLY ON AS-BUILT RECORDS.
 - WELDS AND/OR COUPLINGS DEFINING RANDOM PIPE SPOOL LENGTHS ARE FOR REFERENCE ONLY. FINAL WELD OR COUPLING LOCATION IS TO BE DETERMINED BY THE CONTRACTOR.
 - THE MECHANICAL CONTRACTOR TO FIELD VERIFY INTERFACE POINTS BETWEEN EQUIPMENT & PLUMBING FIXTURES IN 3rd FIX (3F SERIES CWP) AND YS YARD STICK BUILT (YS SERIES CWP EQUIPMENT CONNECTIONS) ISOMETRICS PRIOR TO FABRICATION.
 - THE MECHANICAL CONTRACTOR IS TO VERIFY ALL DIMENSIONAL DATA WITH ACTUAL FIELD CONDITIONS PRIOR TO INSTALLATION OF THE SYSTEM.
 - PIPE SUPPORTS SHALL BE FURNISHED AND INSTALLED IN ACCORDANCE WITH THIS DRAWING AND SPECIFICATION LP100-250-EMS-15110. MECHANICAL CONTRACTOR SHALL PROVIDE TEMPORARY SUPPORTS AS REQUIRED TO AID PRESSURE TESTING, INSTALLATION ETC.
 - PIPE SUPPORTS INDICATED ON THE DRAWING MAY BE PART OF AN ASSEMBLY ON SEVERAL ISOMETRICS. REFER TO THE 3D MODEL FOR THE COMPLETE PIPE SUPPORT ASSEMBLY.
 - MECHANICAL CONTRACTOR SHALL NOTE ALL DESIGN CHANGES ON THIS DRAWING AND RETURN IT TO THE CONSTRUCTION WPO FOR AS-BUILT RECORDS.
 - THE BILL OF MATERIAL IS FOR REFERENCE ONLY.
 - SLOPE EQUIVALENTS: 1:27 = 7/16" PER FT, 1:96 = 1/8" PER FT, 1:120 = 1/10" PER FT, 1:192 = 1/16" PER FT, 1:480 = 1/40" PER FT.

NODE:	TFS
BUILDING NO:	Y
CWP NO:	TFS00D005YSPP
MODULE NO:	N/A
SERVICE CODE:	PWP
PIPE SCHEDULE:	315
INSULATION CODE:	108
TRACING TYPE:	ET
ELASTOMER:	NE
HYGIENIC: NO	IMPACT: NO

0	ISSUED FOR CONSTRUCTION	17-APR-2026	DRC	CTK	RRS	N/A	MKF
REV. NO.	DESCRIPTION	DATE	DRWN	CHK	STR	INSTR	QC
						PRCS	
		 EFDEE Engineering PC PROJECT NO. B1LG					
LINE NUMBER		LP1Y 6" SS PWP (315) (108) 014002					
REFERENCE P&ID NUMBER		ISOMETRIC DRAWING NUMBER		REV			
LP1Y-DI-00000014		LP1Y-PWP-014002-16		0			