


N

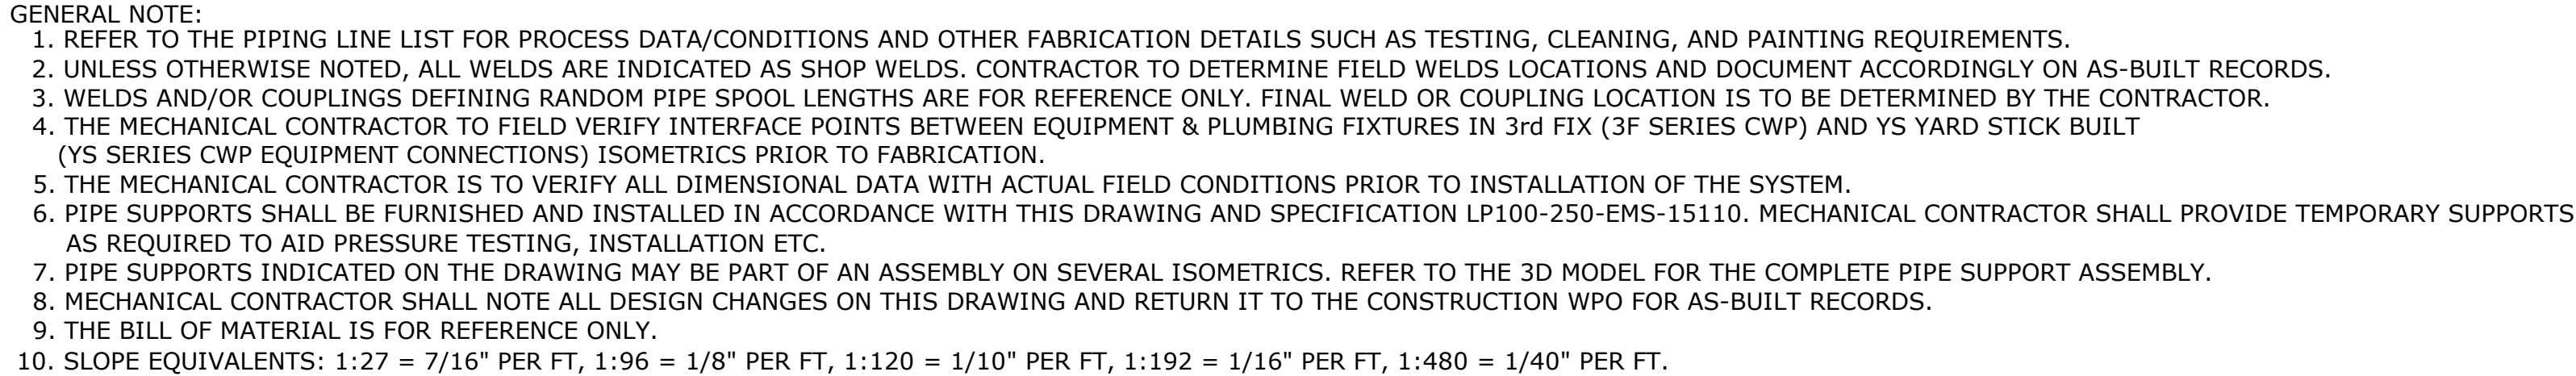

NODE:	TFS	
BUILDING NO:	Y	
CWP NO:	TFS00D003YSPP	
MODULE NO:	N/A	
SERVICE CODE:	STORMP	
PIPE SCHEDULE:	315	
INSULATION CODE:	108	
TRACING TYPE:	ET	
ELASTOMER:	NE	
HYGIENIC: NO	IMPACT: NO	

0	ISSUED FOR CONSTRUCTION	11-FEB-2026	LIJ	CTK	RRS	N/A	MKF
REV. NO.	DESCRIPTION	DATE	DRWN	CHK	STR	N/A INSTR PRCS	QC

			
LINE NUMBER LP1Y 4" SS STORMP (315) (108) 100412		EFDEE Engineering PC PROJECT NO. B1LG	
REFERENCE P&ID NUMBER LP1Y-DI-20000100		ISOMETRIC DRAWING NUMBER LP1Y-STORMP-100412-01	
		REV 0	