


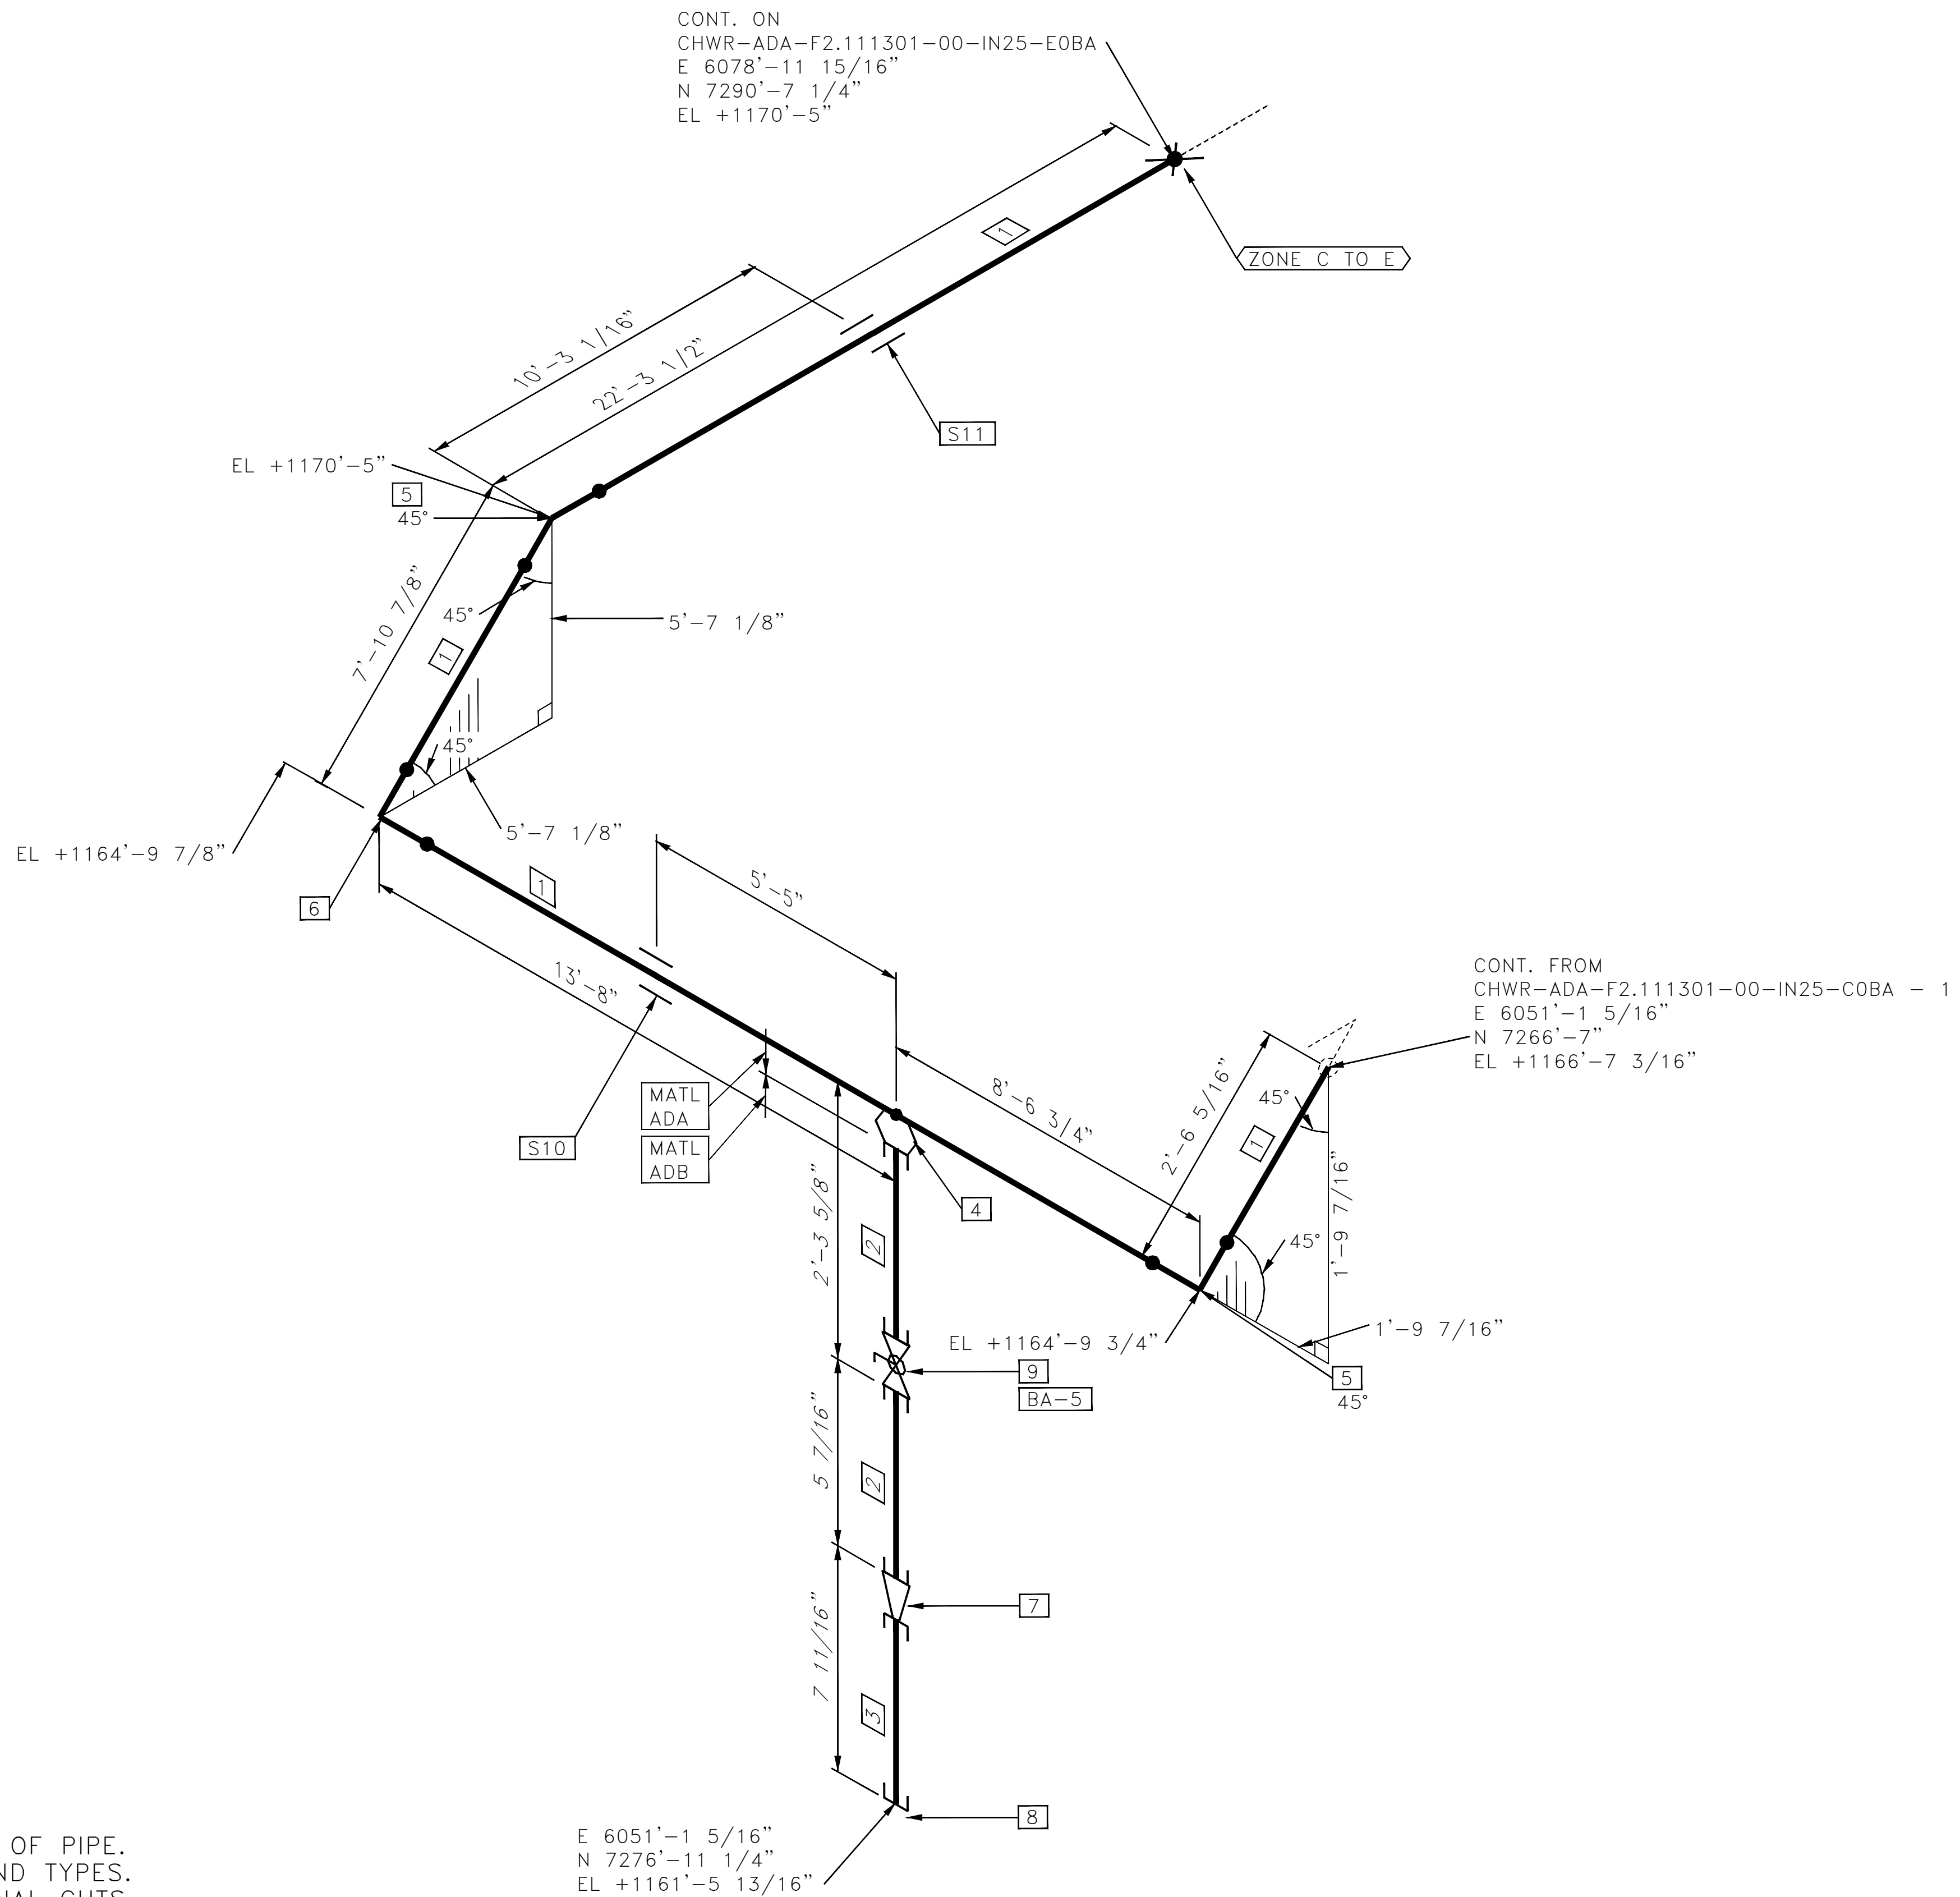

1. FFW- LEAVE 1'-0" EXTRA LENGTH OF PIPE.
2. VERIFY ALL SUPPORT LOCATIONS AND TYPES.
3. VERIFY ALL DIMENSIONS BEFORE FINAL CUTS.

**ISSUED FOR  
CONSTRUCTION**

| PIPE LOCATION                                 |     | PIPE INFO       |               |                      |                    | MARK | DATE     | REVISION                | BY | AP | <div></div> | INTEL PROJECT MOD 2      |                                   |  |             |  |
|-----------------------------------------------|-----|-----------------|---------------|----------------------|--------------------|------|----------|-------------------------|----|----|--------------------------------------------------------------------------------------------------|--------------------------|-----------------------------------|--|-------------|--|
| <input checked="" type="checkbox"/> YARD PIPE | WP# | SERVICE         | CHWR          | DESIGN CODE          | ASME B31.3 – CAT D | 0    | 05/31/24 | ISSUED FOR CONSTRUCTION | QD | JB |                                                                                                  | PIPING ISOMETRIC         |                                   |  |             |  |
| <input type="checkbox"/> TRESTLE PIPE         |     | PIPE SPEC       | ADA           | NDE REQUIREMENTS     | N/A                |      |          |                         |    |    |                                                                                                  |                          |                                   |  |             |  |
| CONSTRUCTION ZONE: C                          |     | DESIGN PRESSURE | 125 PSI       | COATING SPEC         | NONE               |      |          |                         |    |    |                                                                                                  | WORK GROUP:MECH          |                                   |  |             |  |
| LEVEL: OBA                                    |     | DESIGN TEMP.    | −20°F / 350°F | INSULATION SPEC      | TYPE I             |      |          |                         |    |    |                                                                                                  | UPN:CHILLED WATER RETURN |                                   |  |             |  |
| LOCATION: SUT TRENCH                          |     | TEST PRESSURE   | 188 PSI       | INSULATION THICKNESS | 2.5"               |      |          |                         |    |    |                                                                                                  | DES: QD                  |                                   |  |             |  |
|                                               |     |                 |               |                      |                    |      |          |                         |    |    |                                                                                                  | DATE:05/24/24            |                                   |  |             |  |
|                                               |     |                 |               |                      |                    |      |          |                         |    |    | UPN#: 111                                                                                        |                          |                                   |  |             |  |
|                                               |     |                 |               |                      |                    |      |          |                         |    |    | DR: RL                                                                                           |                          | SCALE: N.T.S.                     |  | DWG. 2 OF 2 |  |
|                                               |     |                 |               |                      |                    |      |          |                         |    |    | CH: RJ                                                                                           |                          | DWG. NO.:                         |  |             |  |
|                                               |     |                 |               |                      |                    |      |          |                         |    |    | AP: CK                                                                                           |                          | CHWR−ADA−F2.111301−00−IN25−C0BA−2 |  | REV. 0      |  |